

DEVELOPER & BUILDER PACKAGE

Sadler Farms

A lakeside development opportunity on Lake Wheeler

CONTENTS

Site facts
Sheet 1 — Conceptual Lot Layout
Sheet 2 — Boundary Survey
Sheet 3 — Boundary Survey with Topography

Issued October 2026. Sadler Farms represents a potential development opportunity. All plans, layouts, uses and renderings are conceptual and illustrative only, are not engineered, and are subject to planning, engineering, governmental approvals and permitting. Acreage, shoreline length and travel times are approximate and should be independently verified.

SITE FACTS

The property at a glance

Location	Davis Road & Snake Road, Limestone County, Alabama
Size	Approximately 300 acres
Waterfront	More than one mile along the Tennessee River's Wheeler Reservoir, east of the Elk River confluence; portions are direct waterfront and portions are continuous to vertical TVA bluff land
Coves	Two protected coves; one is suitable for possible marina development
Access	Two county roads
Drive times	About 15 minutes to Athens and 25 minutes to Huntsville
Current use	Pasture, hay fields and mature hardwood forest; held by one family for more than 70 years
Concept program	Approximately 300 homesites (townhomes to one-acre estate lots), a possible community marina, trails and open space
Shoreline	Lake Wheeler is a TVA reservoir; docks and other shoreline structures require TVA Section 26a approval
Zoning & entitlements	To be confirmed

Sadler Farms represents a potential development opportunity. All plans, layouts, uses and renderings are conceptual and illustrative only, are not engineered, and are subject to planning, engineering, governmental approvals and permitting. Acreage, shoreline length and travel times are approximate and should be independently verified.



Sadler Farms


LAKE WHEELER · LIMESTONE COUNTY, AL

Conceptual Lot Layout

Illustrative street and lot arrangement for approximately 300 homesites, with waterfront, lake-view and interior lots around preserved open space.

CONCEPTUAL — NOT FOR CONSTRUCTION. NOT A SURVEY. Sadler Farms represents a potential development opportunity. All plans, layouts, uses and renderings are conceptual and illustrative only, are not engineered, and are subject to planning, engineering, governmental approvals and permitting. Acreage, shoreline length and travel times are approximate and should be independently verified.

Issued October 2026

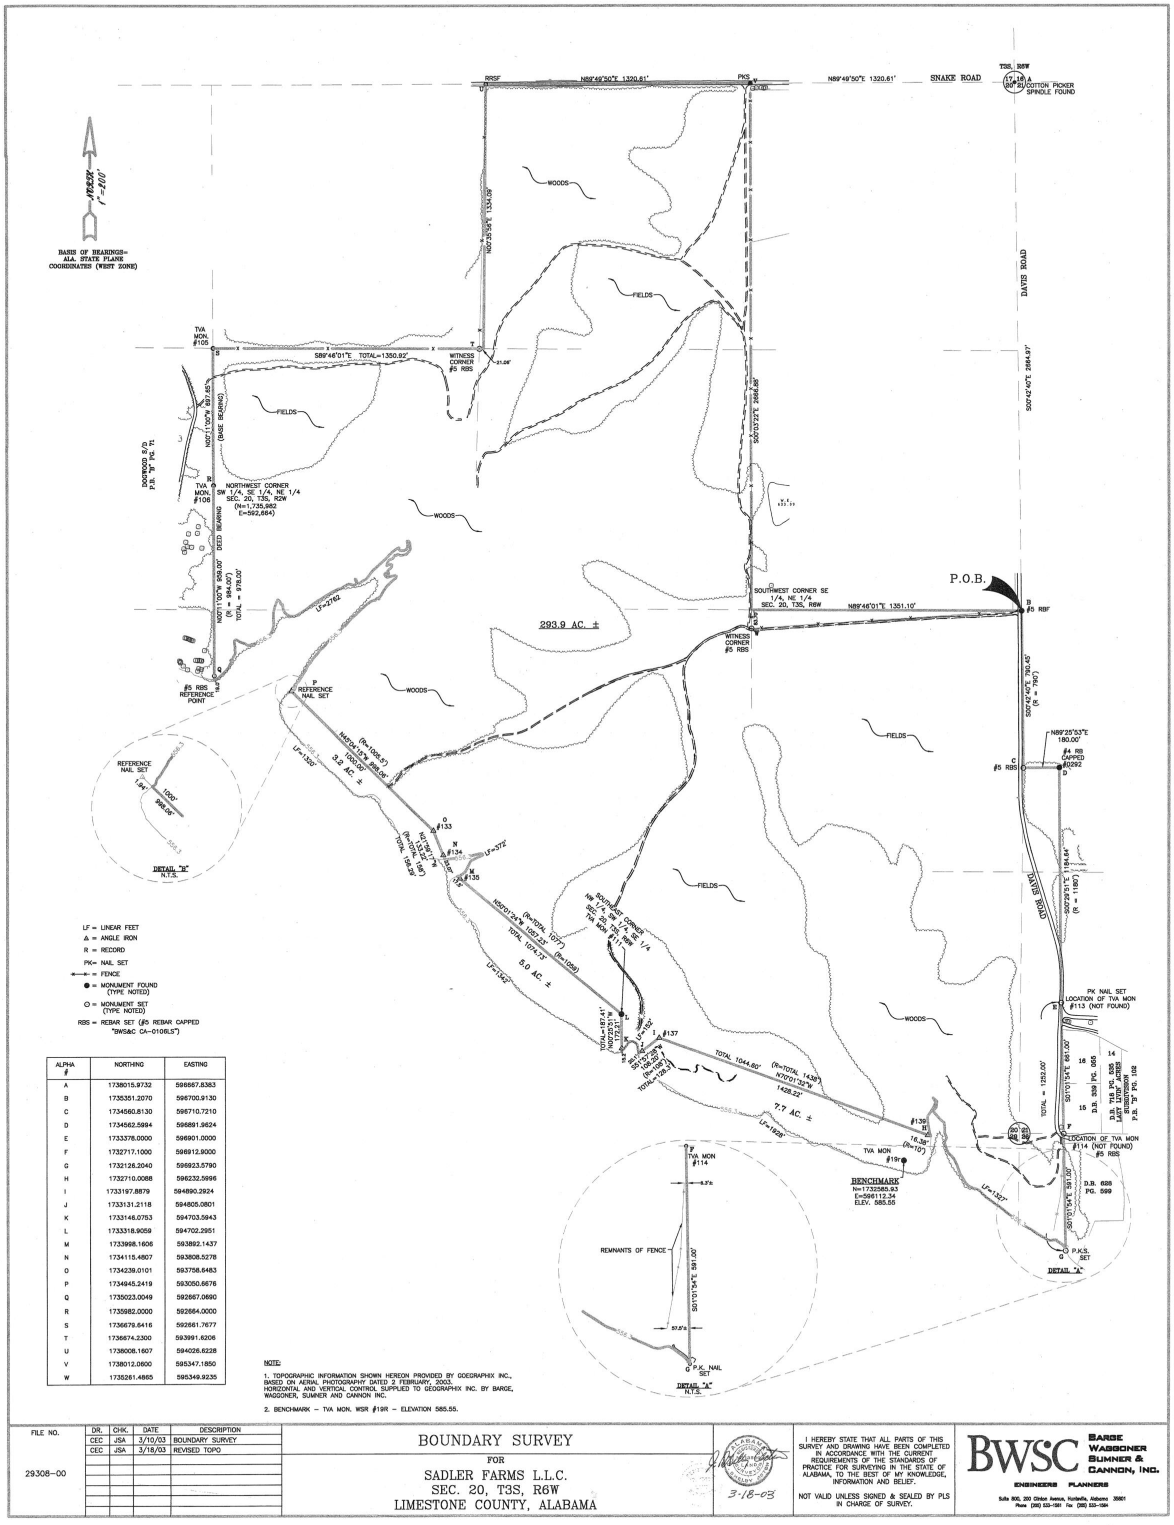

ALPHA #	NORTHING	EASTING
A	1738015.9732	596667.8383
B	1735351.2070	596700.9130
C	1734560.8130	596710.7210
D	1734562.5984	596891.9624
E	1733378.0000	596901.0000
F	1732717.1000	596912.9000
G	1732128.2040	596923.5790
H	1732710.0068	596232.5996
I	1733197.8879	594890.2924
J	1733131.2118	594805.0801
K	1733146.0753	594703.5943
L	1733318.9059	594702.2951
M	1733998.1606	593892.1437
N	1734115.4807	593808.5278
O	1734239.0101	593758.6483
P	1734945.2419	593050.6676
Q	1735023.0049	592667.0690
R	1735982.0000	592664.0000
S	1736679.6416	592661.7677
T	1736674.2300	593991.6206
U	1738008.1607	594026.6228
V	1738012.0600	595347.1850
W	1735281.4865	595349.9235

FILE NO.	DR.	CHK.	DATE	DESCRIPTION
29308-00	CEC	JSA	3/10/03	BOUNDARY SURVEY
	CEC	JSA	3/18/03	REVISED TOPO

BOUNDARY SURVEY
FOR
SADLER FARMS L.L.C.
SEC. 20, T3S, R6W
LIMESTONE COUNTY, ALABAMA

3-18-03

I HEREBY STATE THAT ALL PARTS OF THIS SURVEY AND DRAWING HAVE BEEN COMPLETED IN ACCORDANCE WITH THE CURRENT REQUIREMENTS OF THE STANDARDS OF PRACTICE FOR SURVEYING IN THE STATE OF ALABAMA, TO THE BEST OF MY KNOWLEDGE, INFORMATION AND BELIEF.

NOT VALID UNLESS SIGNED & SEALED BY PLS IN CHARGE OF SURVEY.

BWSC BARGE WAGGONER SUMNER & CANNON, INC.
ENGINEERS PLANNERS


Sadler Farms
LAKE WHEELER · LIMESTONE COUNTY, AL

Boundary Survey

Signed boundary survey of the property, dated March 10, 2003. Prepared for Sadler Farms LLC by Barge Waggoner Sumner & Cannon (BWSC); Sec. 20, T3S, R6W, Limestone County, Alabama. Original scale 1" = 200'.

REDUCED REFERENCE COPY — NOT TO SCALE. Refer to the full-size signed survey at sadlerfarmsllc.com/developers.

Issued October 2026

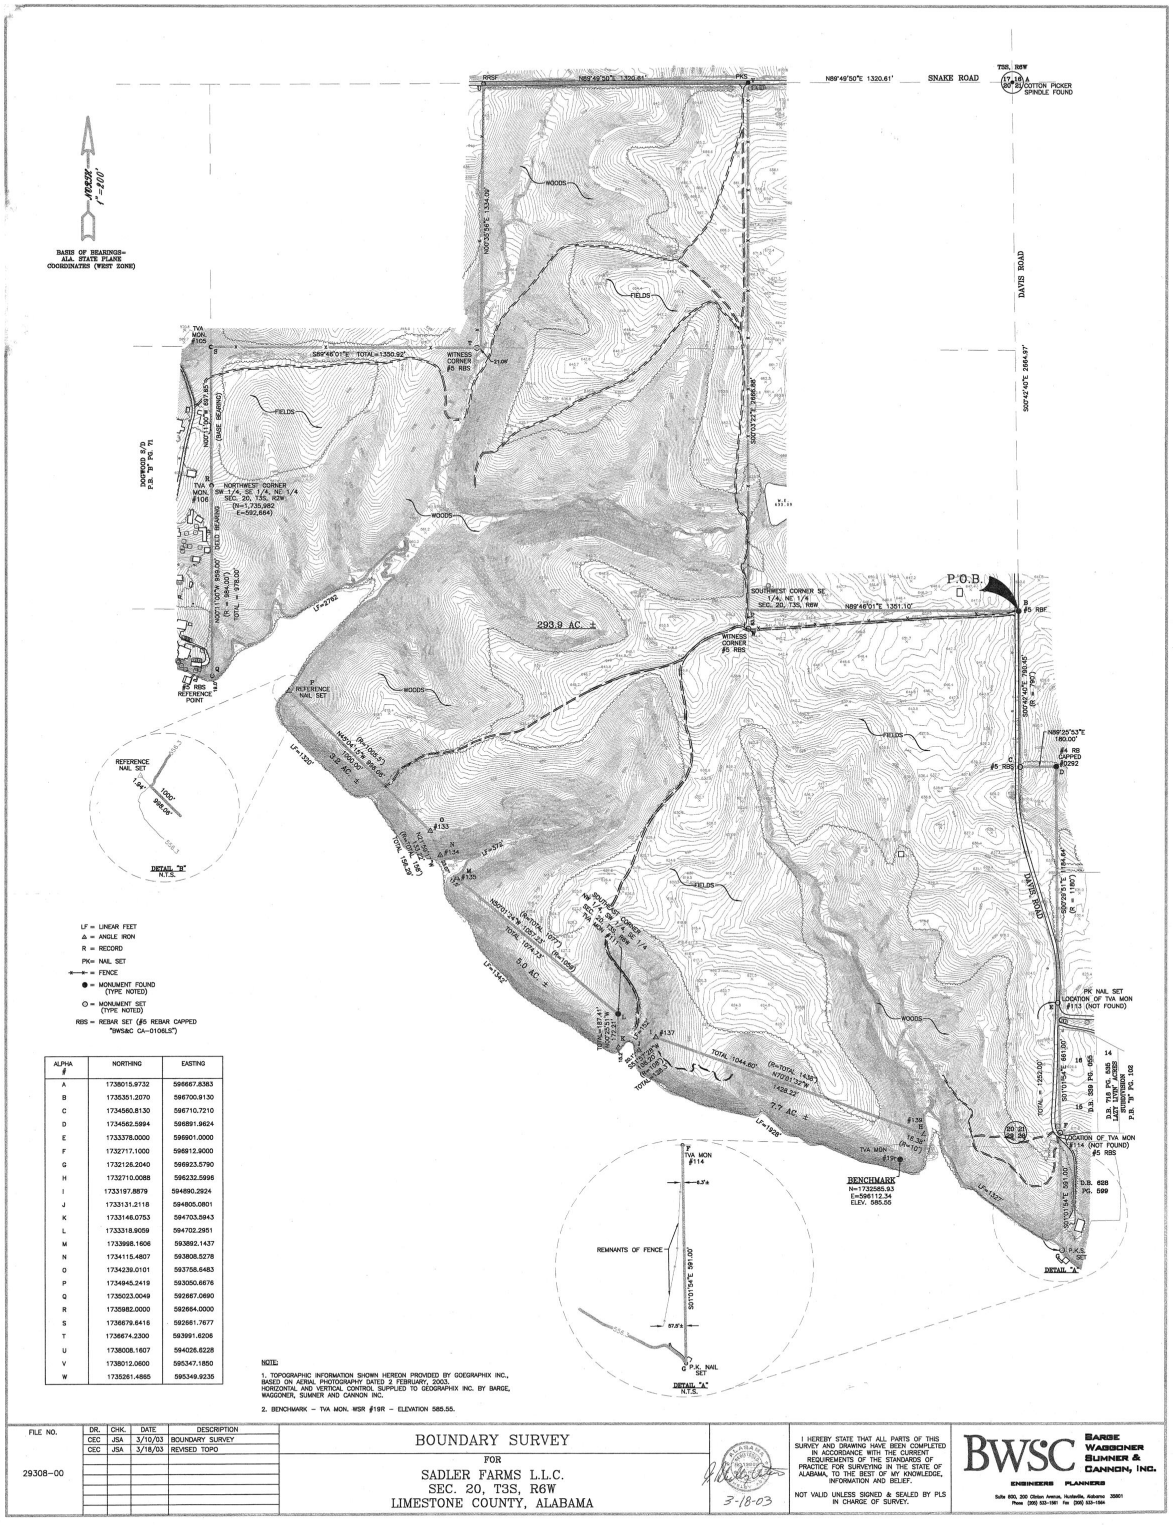

ALPHA #	NORTHING	EASTING
A	1738015.9732	594667.8383
B	1735351.2070	596700.8130
C	1734560.8130	596710.7210
D	1734562.5994	596891.9624
E	1733378.0000	596901.0000
F	1732717.1000	596912.9000
G	1732126.2040	596923.5790
H	1732710.0088	596232.5996
I	1733197.8879	594890.2924
J	1733131.2118	594805.0801
K	1733146.0753	594703.5943
L	1733318.9059	594702.2951
M	1733998.1606	593892.1437
N	1734115.4807	593808.5278
O	1734239.0101	593758.6483
P	1734945.2419	593050.6676
Q	1735023.0049	592667.0690
R	1735982.0000	592664.0000
S	1736679.6416	592661.7677
T	1736674.2300	593991.6206
U	1738008.1607	594026.6228
V	1738012.0600	595347.1850
W	1735261.4865	595349.9235

DR.	CHK.	DATE	DESCRIPTION
CEC	JSA	3/10/03	BOUNDARY SURVEY
CEC	JSA	3/18/03	REVISED TOPO

Sadler Farms

LAKE WHEELER · LIMESTONE COUNTY, AL

Boundary Survey with Topography

The same survey with topographic contours, revised March 18, 2003. Prepared for Sadler Farms LLC by Barge Waggoner Sumner & Cannon (BWSC); Sec. 20, T3S, R6W, Limestone County, Alabama. Original scale 1" = 200'.

REDUCED REFERENCE COPY — NOT TO SCALE. Refer to the full-size signed survey at sadlerfarmsllc.com/developers.

Issued October 2026