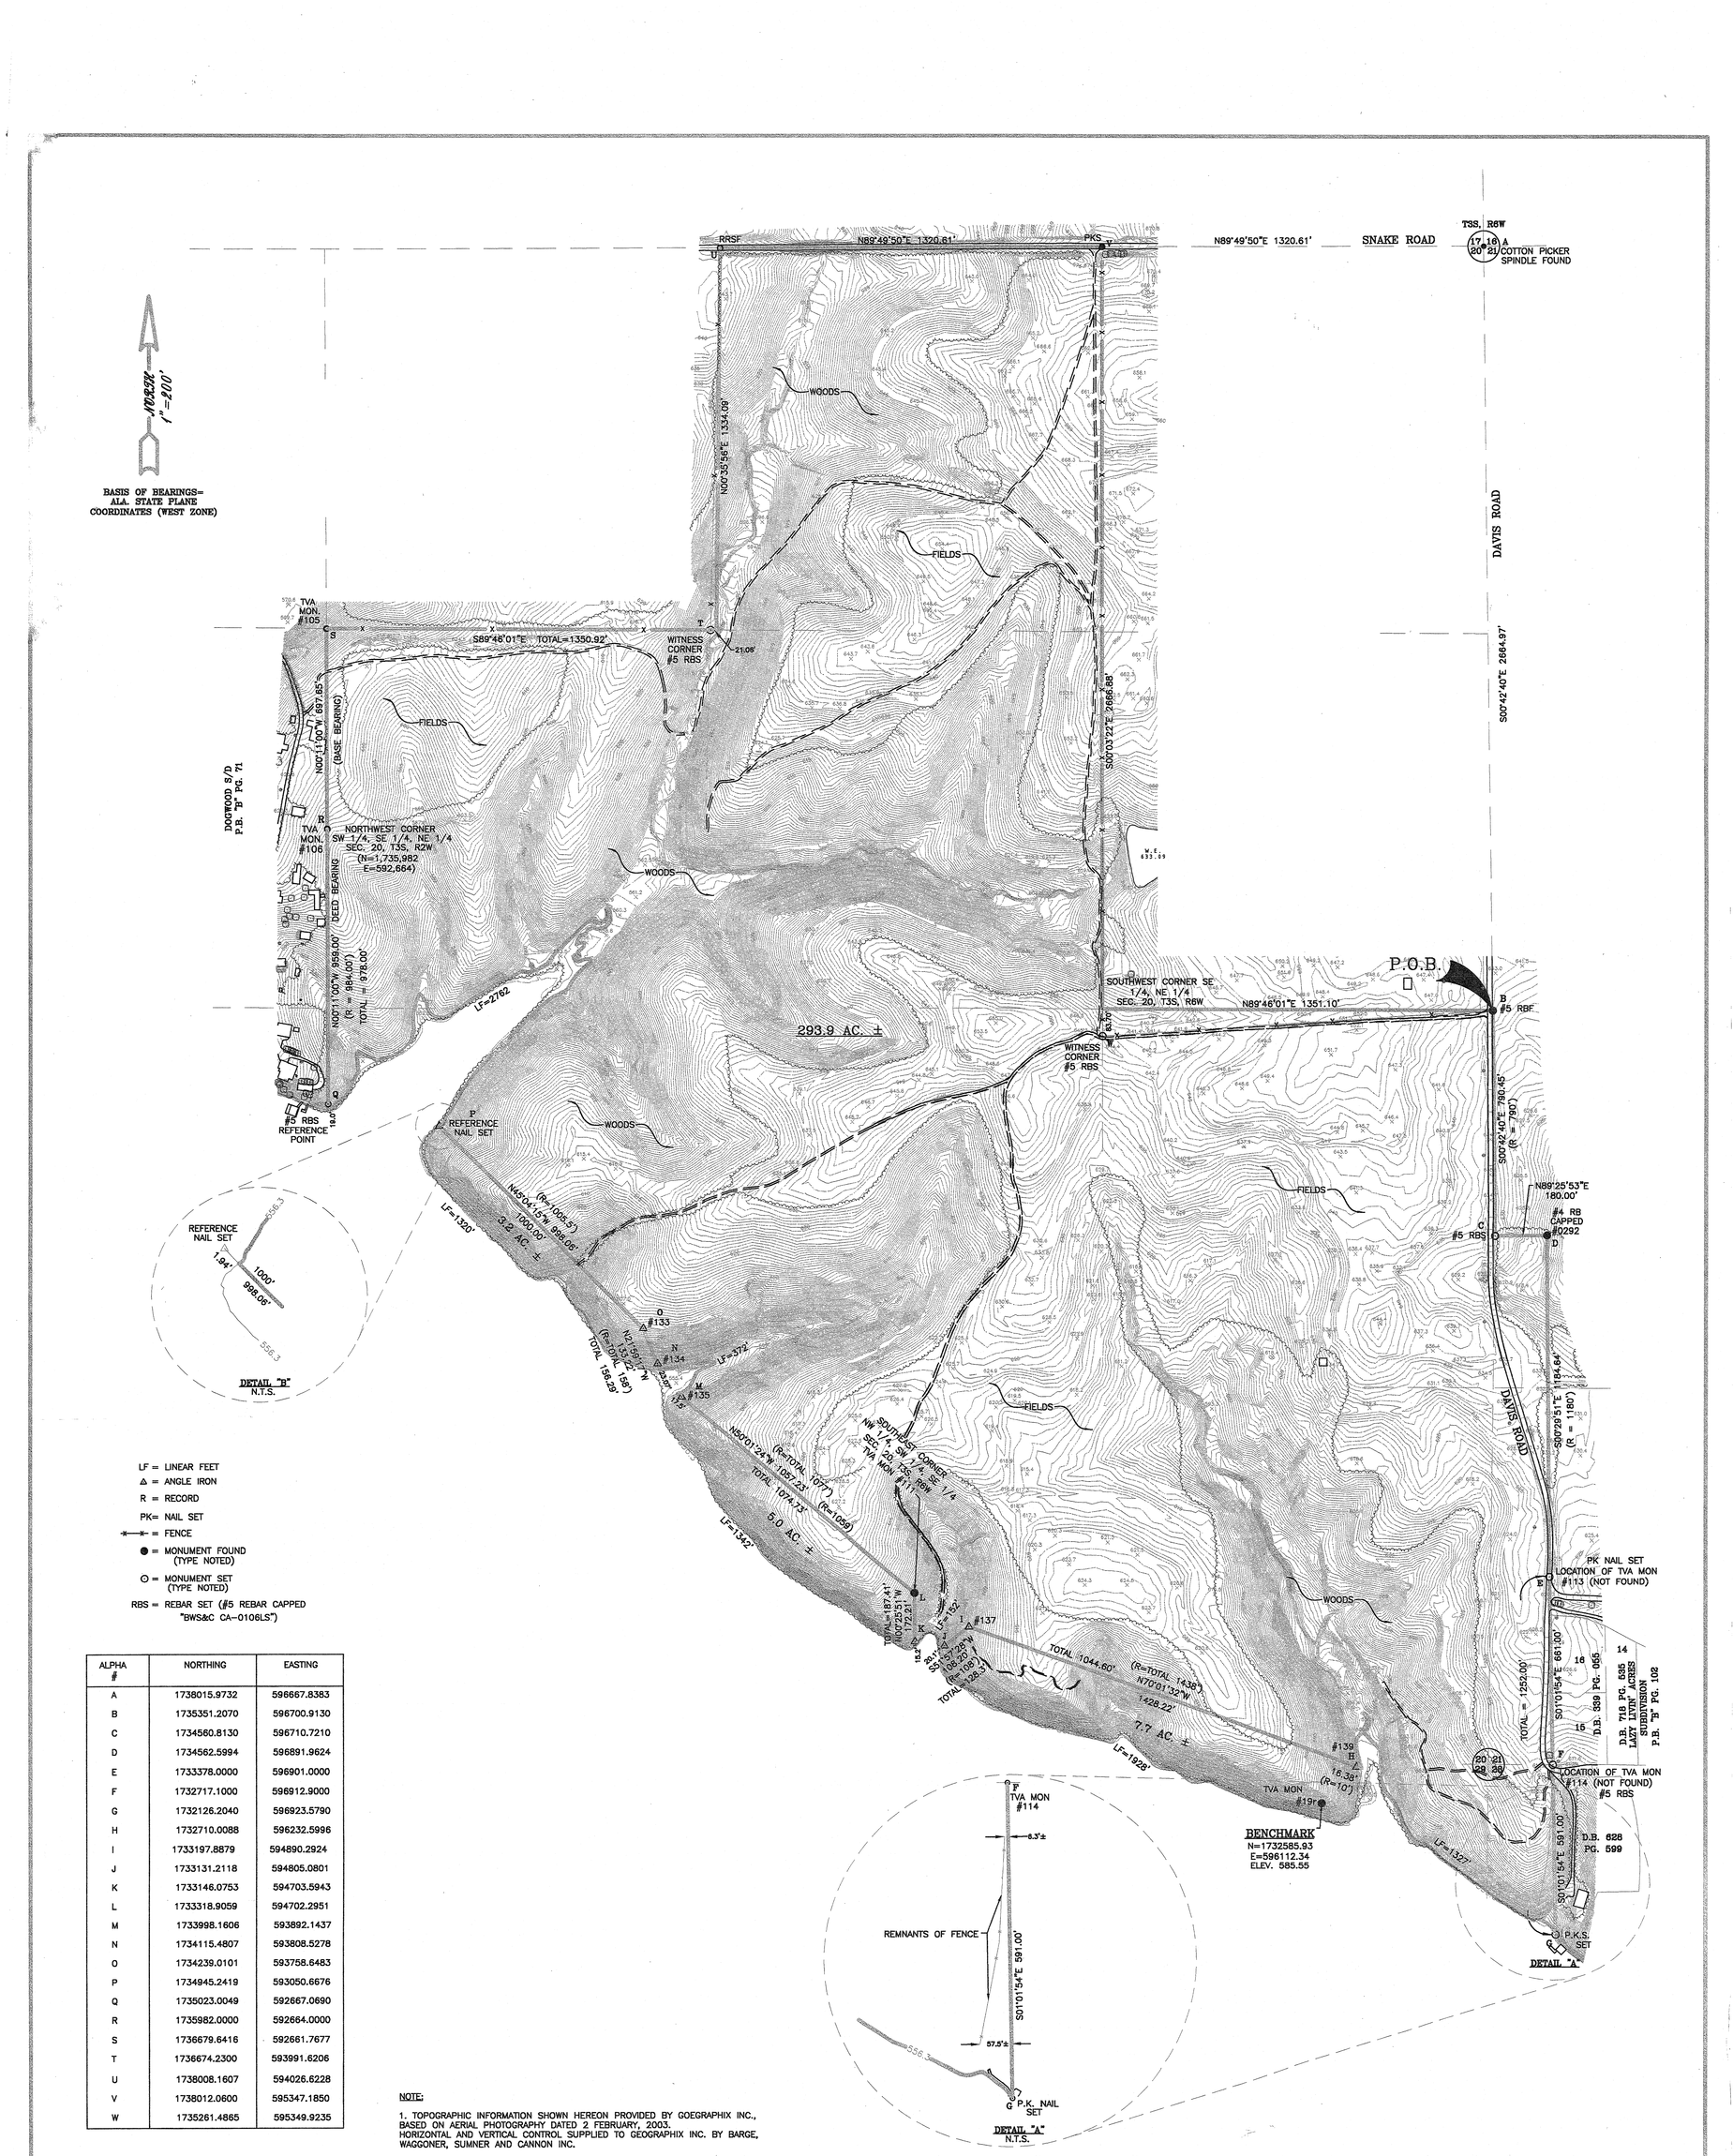


LF = LINEAR FEET
△ = ANGLE IRON
R = RECORD
PK= NAIL SET
-x-x- = FENCE
● = MONUMENT FOUND (TYPE NOTED)
○ = MONUMENT SET (TYPE NOTED)
RBS = REBAR SET (#5 REBAR CAPPED "BWS&C CA-0106LS")

ALPHA #	NORTHING	EASTING
A	1738015.9732	596667.8383
B	1735351.2070	596700.9130
C	1734560.8130	596710.7210
D	1734562.5994	596891.9624
E	1733378.0000	596901.0000
F	1732717.1000	596912.9000
G	1732126.2040	596923.5790
H	1732710.0088	596232.5996
I	1733197.8879	594890.2924
J	1733131.2118	594805.0801
K	1733146.0753	594703.5943
L	1733318.9059	594702.2951
M	1733998.1606	593892.1437
N	1734115.4807	593808.5278
O	1734239.0101	593758.6483
P	1734945.2419	593050.6676
Q	1735023.0049	592667.0690
R	1735982.0000	592664.0000
S	1736679.6416	592661.7677
T	1736674.2300	593991.6206
U	1738008.1607	594026.6228
V	1738012.0600	595347.1850
W	1735261.4865	595349.9235

NOTE:

1. TOPOGRAPHIC INFORMATION SHOWN HEREON PROVIDED BY GOEGRAPHIX INC., BASED ON AERIAL PHOTOGRAPHY DATED 2 FEBRUARY, 2003. HORIZONTAL AND VERTICAL CONTROL SUPPLIED TO GEOGRAPHIX INC. BY BARGE, WAGGONER, SUMNER AND CANNON INC.

2. BENCHMARK – TVA MON. WSR #19R – ELEVATION 585.55.

FILE NO.	DR.	CHK.	DATE	DESCRIPTION
	CEC	JSA	3/10/03	BOUNDARY SURVEY
	CEC	JSA	3/18/03	REVISED TOPO
29308-00				

BOUNDARY SURVEY

FOR

SADLER FARMS L.L.C.
SEC. 20, T3S, R6W
LIMESTONE COUNTY, ALABAMA

ALABAMA REGISTERED LAND SURVEYOR 19391 JAMES A. SADLER

3-18-03

I HEREBY STATE THAT ALL PARTS OF THIS SURVEY AND DRAWING HAVE BEEN COMPLETED IN ACCORDANCE WITH THE CURRENT REQUIREMENTS OF THE STANDARDS OF PRACTICE FOR SURVEYING IN THE STATE OF ALABAMA, TO THE BEST OF MY KNOWLEDGE, INFORMATION AND BELIEF.

NOT VALID UNLESS SIGNED & SEALED BY PLS IN CHARGE OF SURVEY.

BWSC BARGE WAGGONER SUMNER & CANNON, INC.
ENGINEERS PLANNERS
Suite 800, 200 Clinton Avenue, Huntsville, Alabama 35801
Phone (205) 533-1561 Fax (205) 533-1564